

République Populaire du Bénin

PROVINCE DU BORGOU

S O U C H E

PRÉFECTURE DE PARAKOU

PERMIS PROVISOIRE D'HABITER N° 54/115

(Loi n° 60-20 du 13 Juillet 1960)
(Décret n° 64-276 du 2 Décembre 1964)

Nom et Prénoms: Piocase de

Nationalité: Parakou

Fil de: /

Et de: /

Age: /

Profession: /

Domicilié à: /


Quartier: /

est autorisé à occuper:

La parcelle n° Non lotie Lot n° en quartier Wobakou Zone n°

Délai de mise en valeur: 6 mois

X/ Grand le 20 août 1984

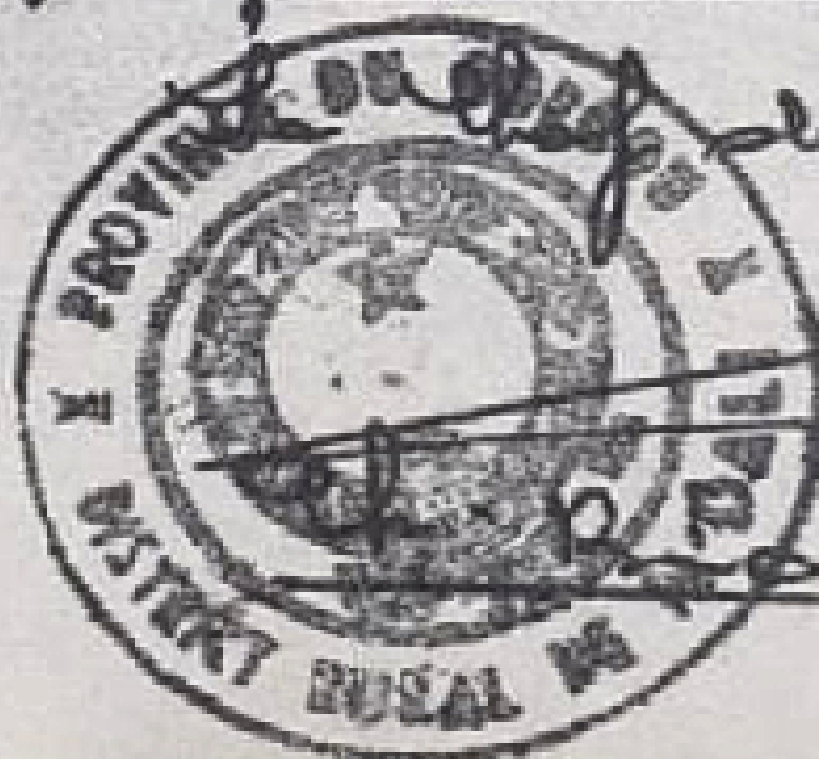


Joseph Nigam

Nigam

Imprimerie Bénin-Typo Tel. 61-22-65 Parakou


TITRE N°

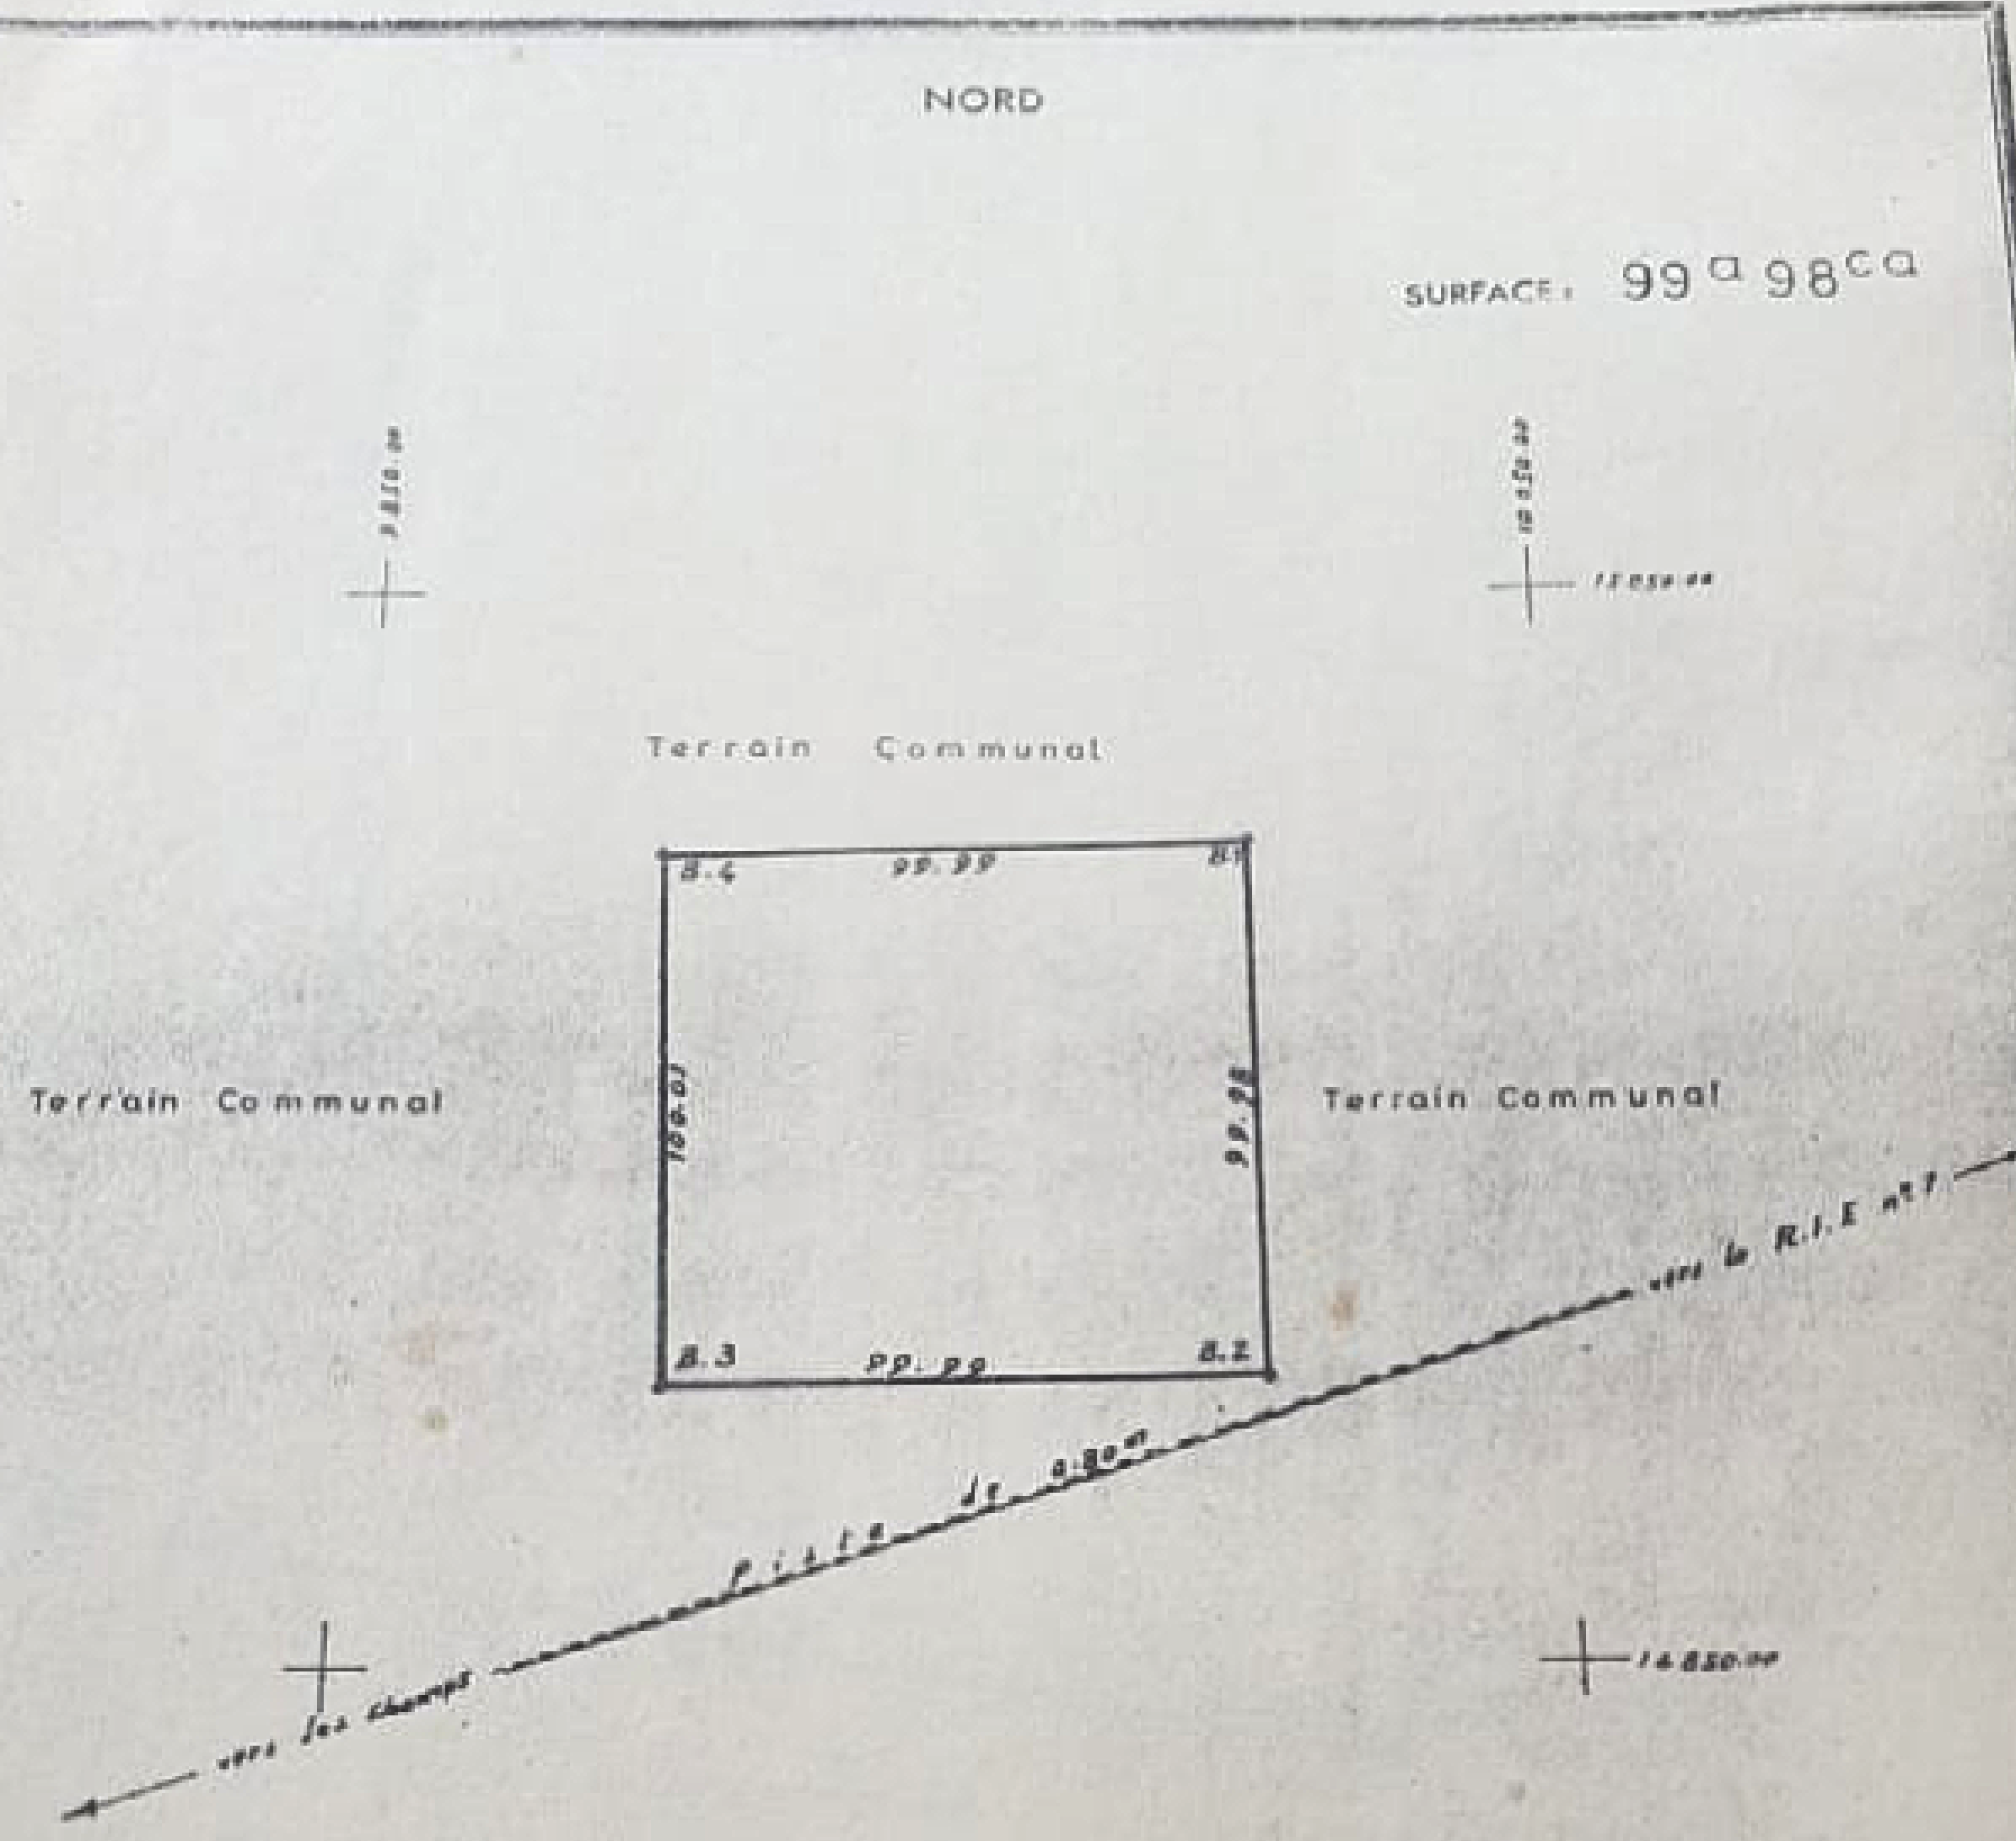

COORDONNÉES

	Y	X
1	15000.00	10000.00
2	14990.04	10001.78
	14898.25	9901.81
	14898.26	9900.02

ECHELLE : 1 / 2 000

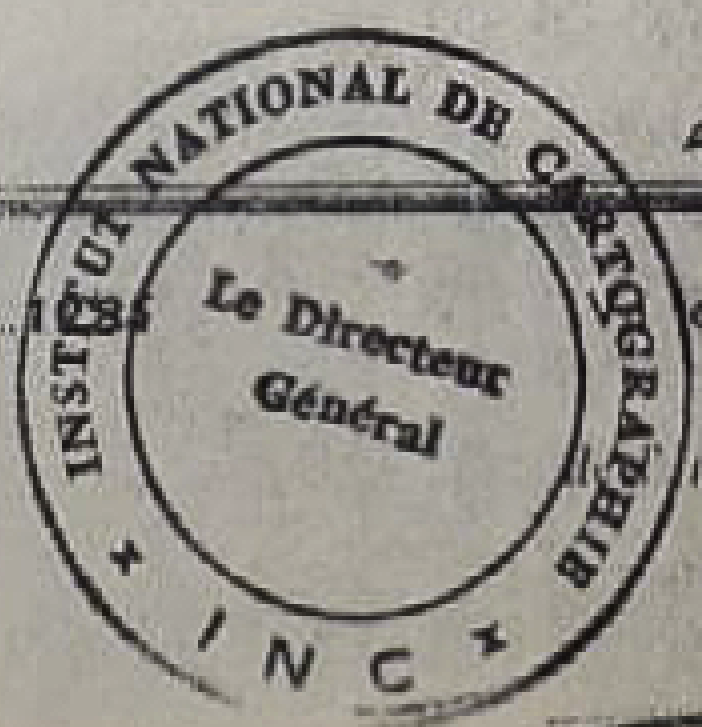

Dessiné par H. D. AYERJI

par le G^e Luc AHINDE Opérateur le 29 - 05 - 1985
vérifié le 21 - 06 - 1985

3 JUIL. 1985

Le Directeur Général
Institut National de Cartographie

Le Directeur du Cadastre

Handwritten signature: N. I. Wali


Handwritten signature

TITRE N°

NORD

SURFACE: 99 a 99 ca


Ecole de Base de Wabakarou
groupe "C"

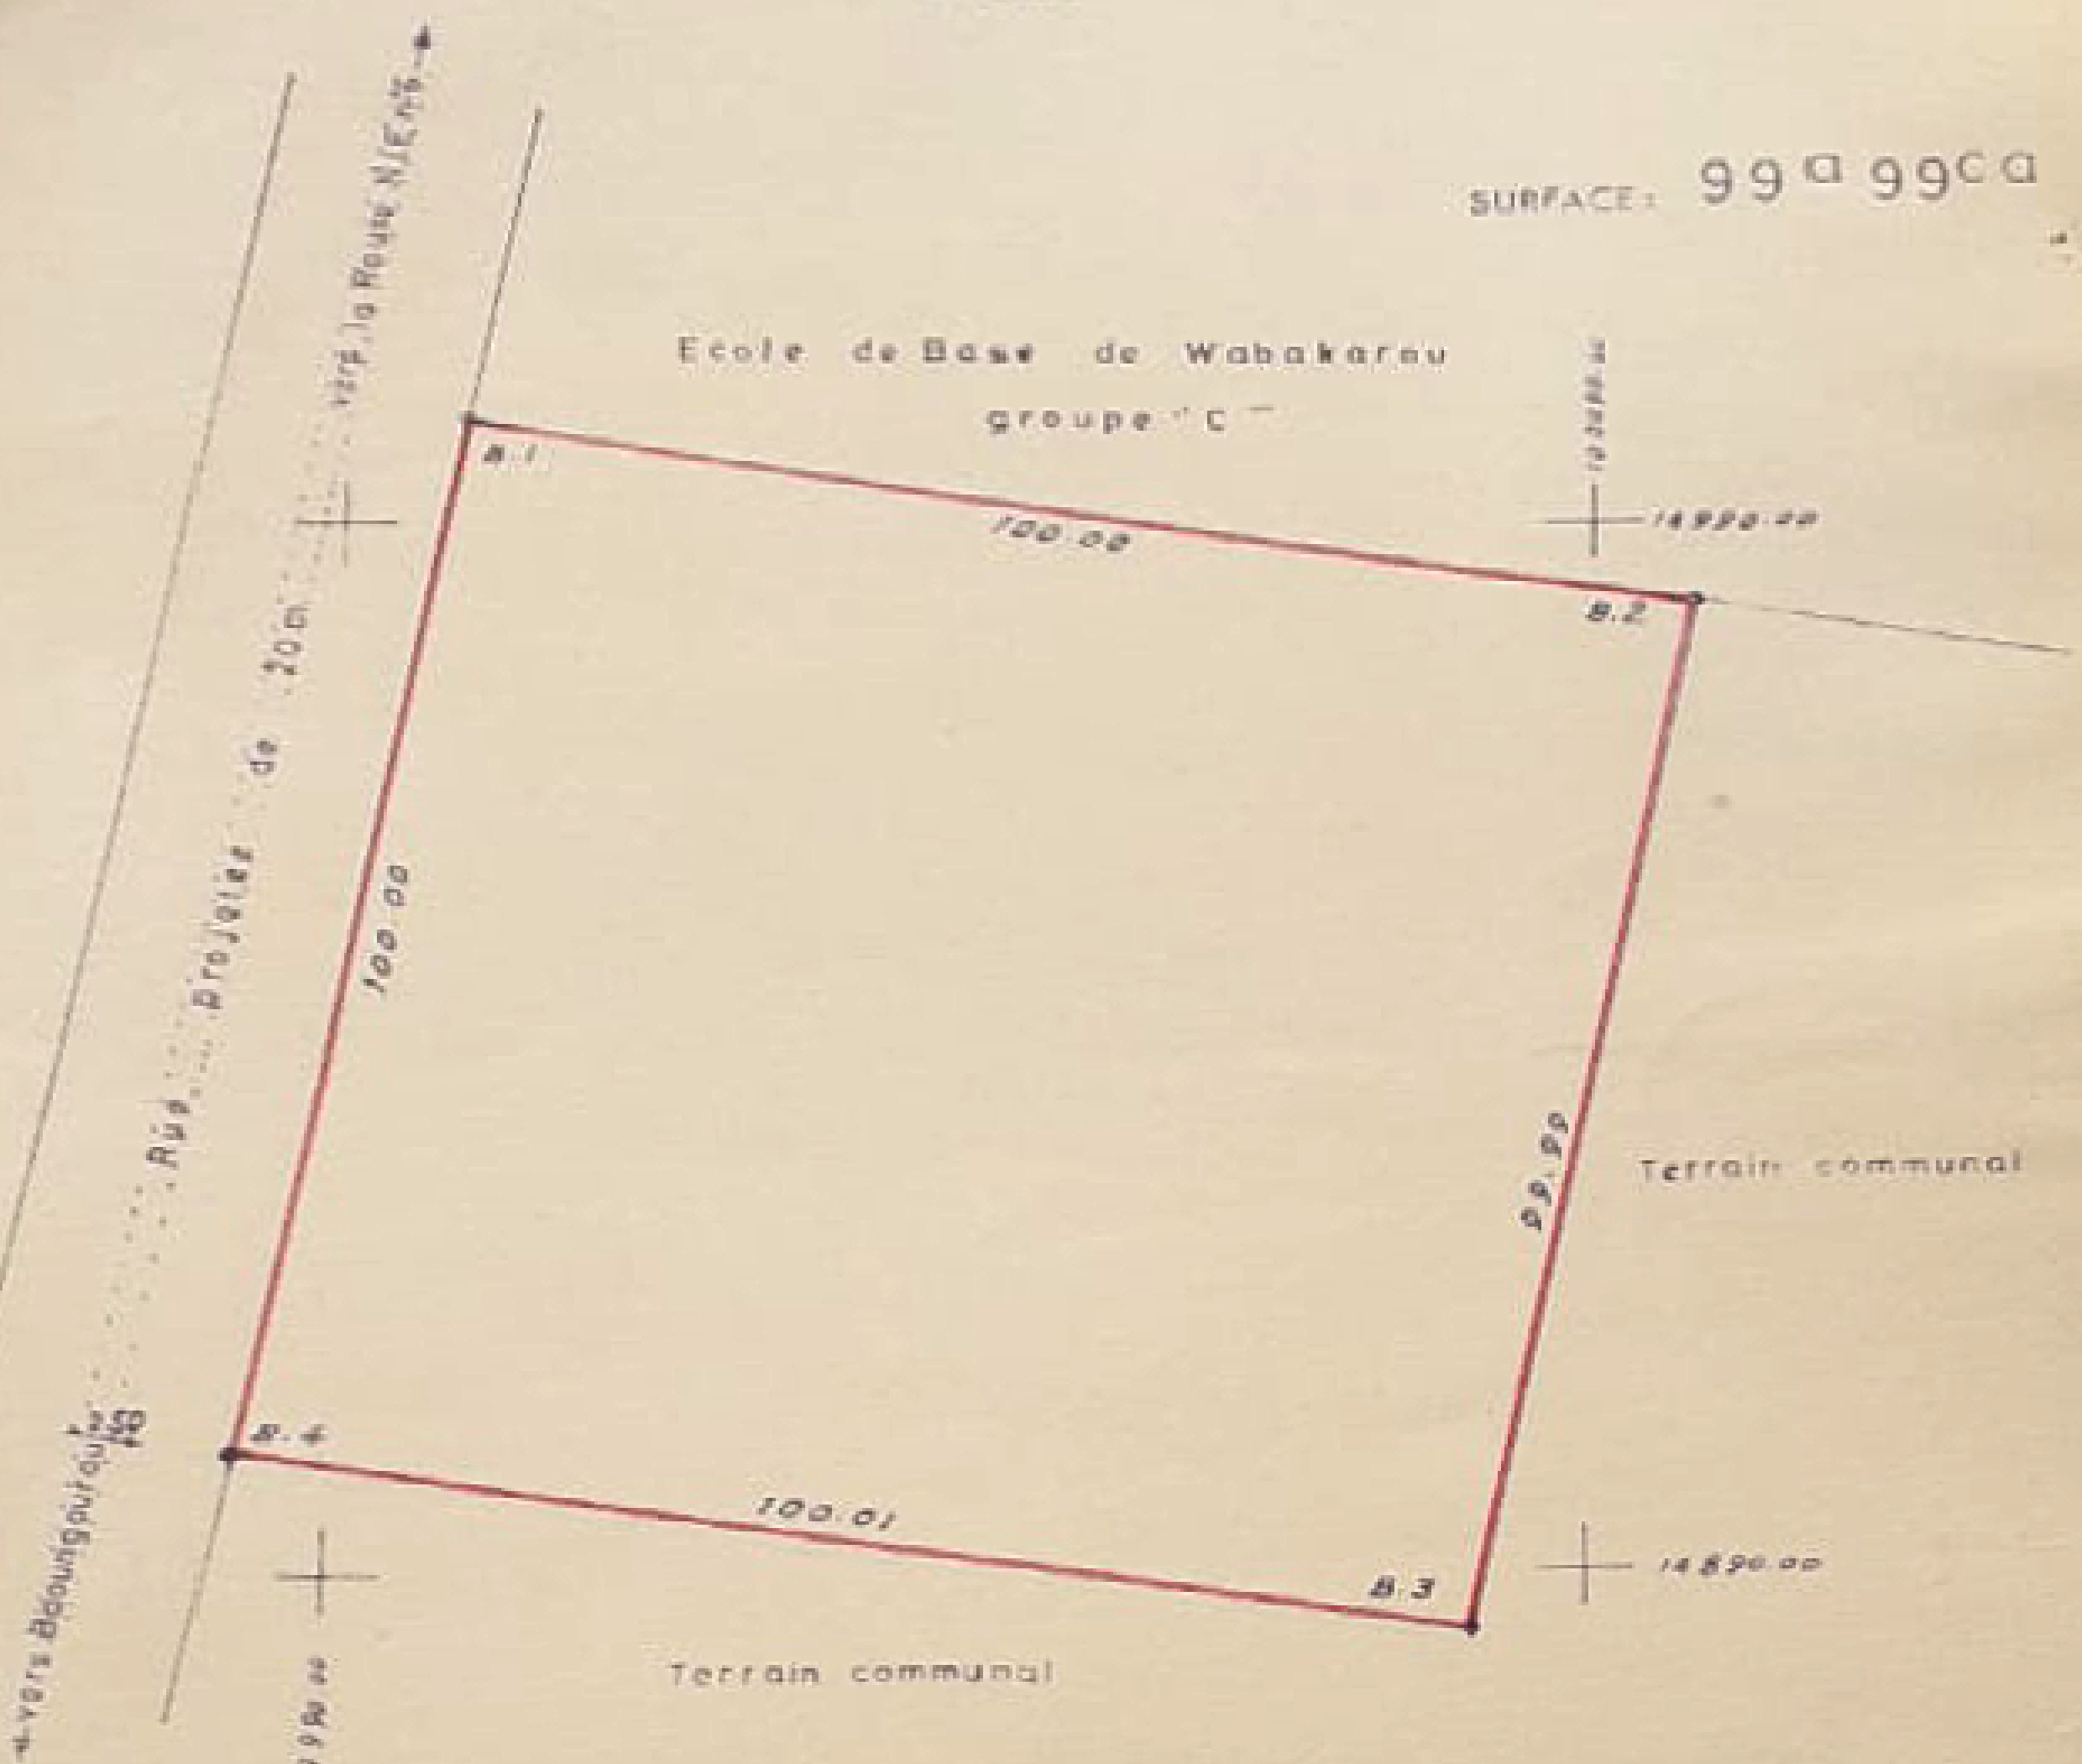

COORDONNEES

	Y	X
1	15000.00	10000.00
2	14982.72	10098.50
3	14884.27	10081.26
4	14901.50	9982.75

ECHELLE: 1/1000

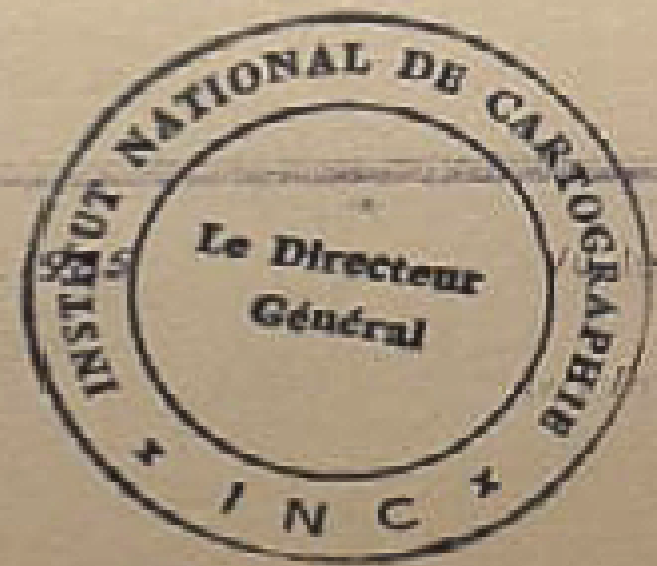

Dessiné par H. D. AIVODJI

3 JUIL. 1985

évalué par le C^{de} LUC AHINDE Op. géomètre le 29 - 05 -

et vérifié le 21 - 06 - 1985

Le Directeur du Service

Joan
B. BOSSOU

N. MOUSSEDIKOU

é d'un terrain sis à N'dali quartier Wabakarou demandé par
L'EVECHE DE PARAKOU